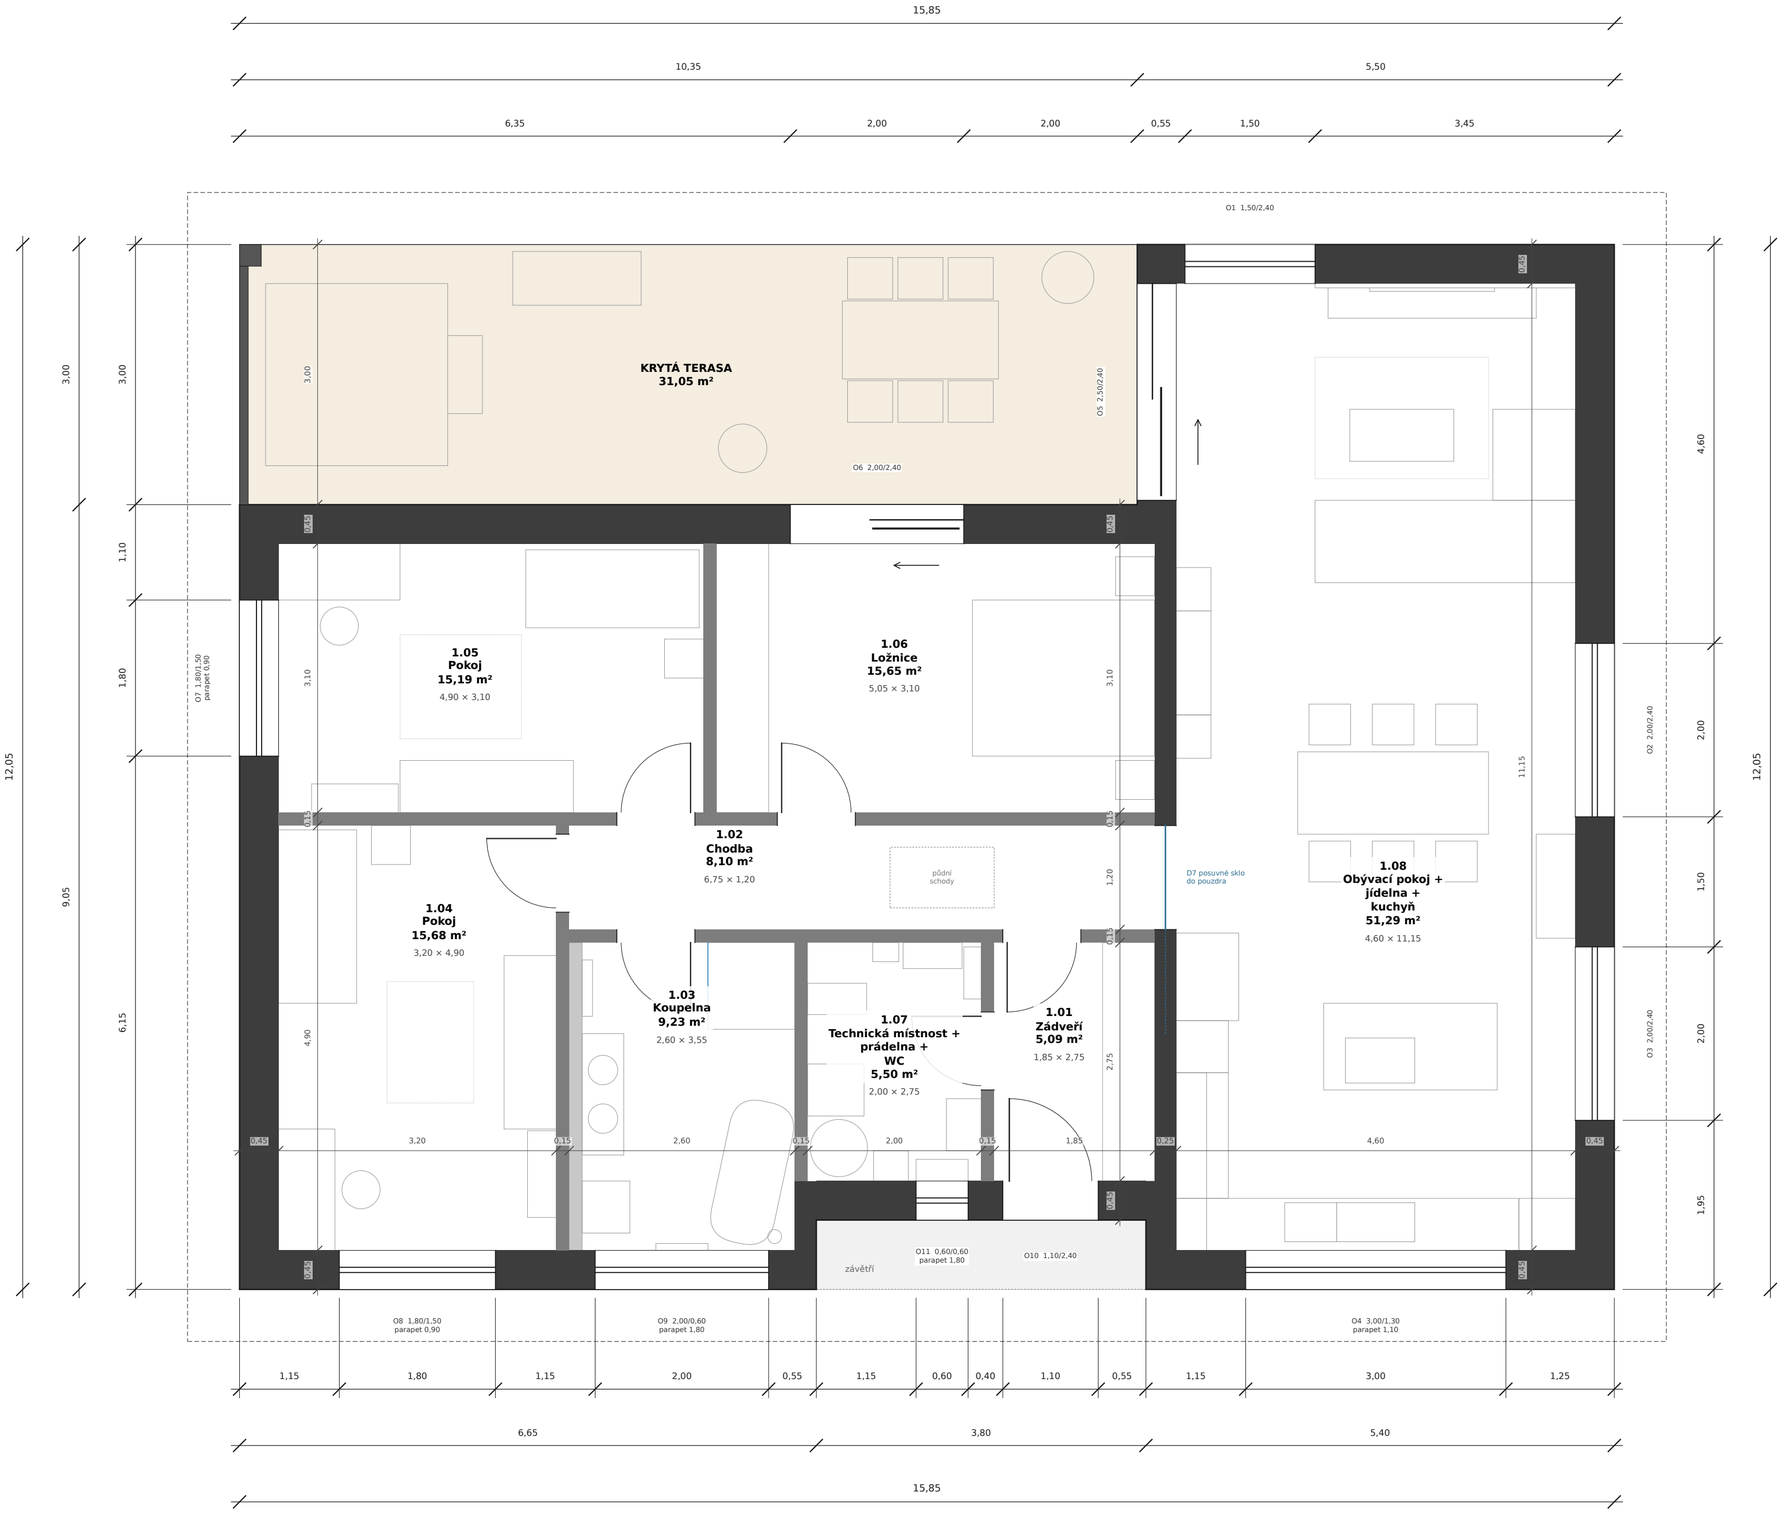


S

PŮDORYS 1. NP

rodinný dům, návrh v6

měřítko 1:50 (A2), na A3 vytisknout 71 %

Místnosti

1.01	Zádveří	5,09 m²
1.02	Chodba	8,10 m²
1.03	Koupelna	9,23 m²
1.04	Pokoj	15,68 m²
1.05	Pokoj	15,19 m²
1.06	Ložnice	15,65 m²
1.07	Technická místnost + prádelna + WC	5,50 m²
1.08	Obývací pokoj + jídelna + kuchyň	51,29 m²
Užitná plocha celkem		**125,73 m²**

Krytá terasa 31,05 m², zastavěná plocha domu 156,90 m²

Legenda

- obvodová a nosná stěna (zateplená, 450 / 250 mm)
- příčka 150 mm
- instalační předstěna (koupelna)
- okno / pevné zasklení (š/v, parapet)
- posuvné dveře do pouzdra
- obrys střechy (přesah 0,60 m)
- nábytek a zařizovací předměty

Poznámky

- Kóty v metrech, vnější řetězce k líci fasády (bez omítky).
- Světlá výška 2,70 m, snížené podhledy 2,55 m.
- Okna: šířka/výška otvoru, parapet od podlahy.
- Vnitřní dveře 80 (otvor 0,90), D7 skleněné posuvné.
- ±0,000 = podlaha = 250,25 m n. m.

Rodinný dům Karviná **1:50**

Půdorys 1. NP – návrh v6

p. č. 2904/26, k. ú. Karviná-město · 25. 10. 2026

Orientační výkres pro rodinu,

není projektová dokumentace.