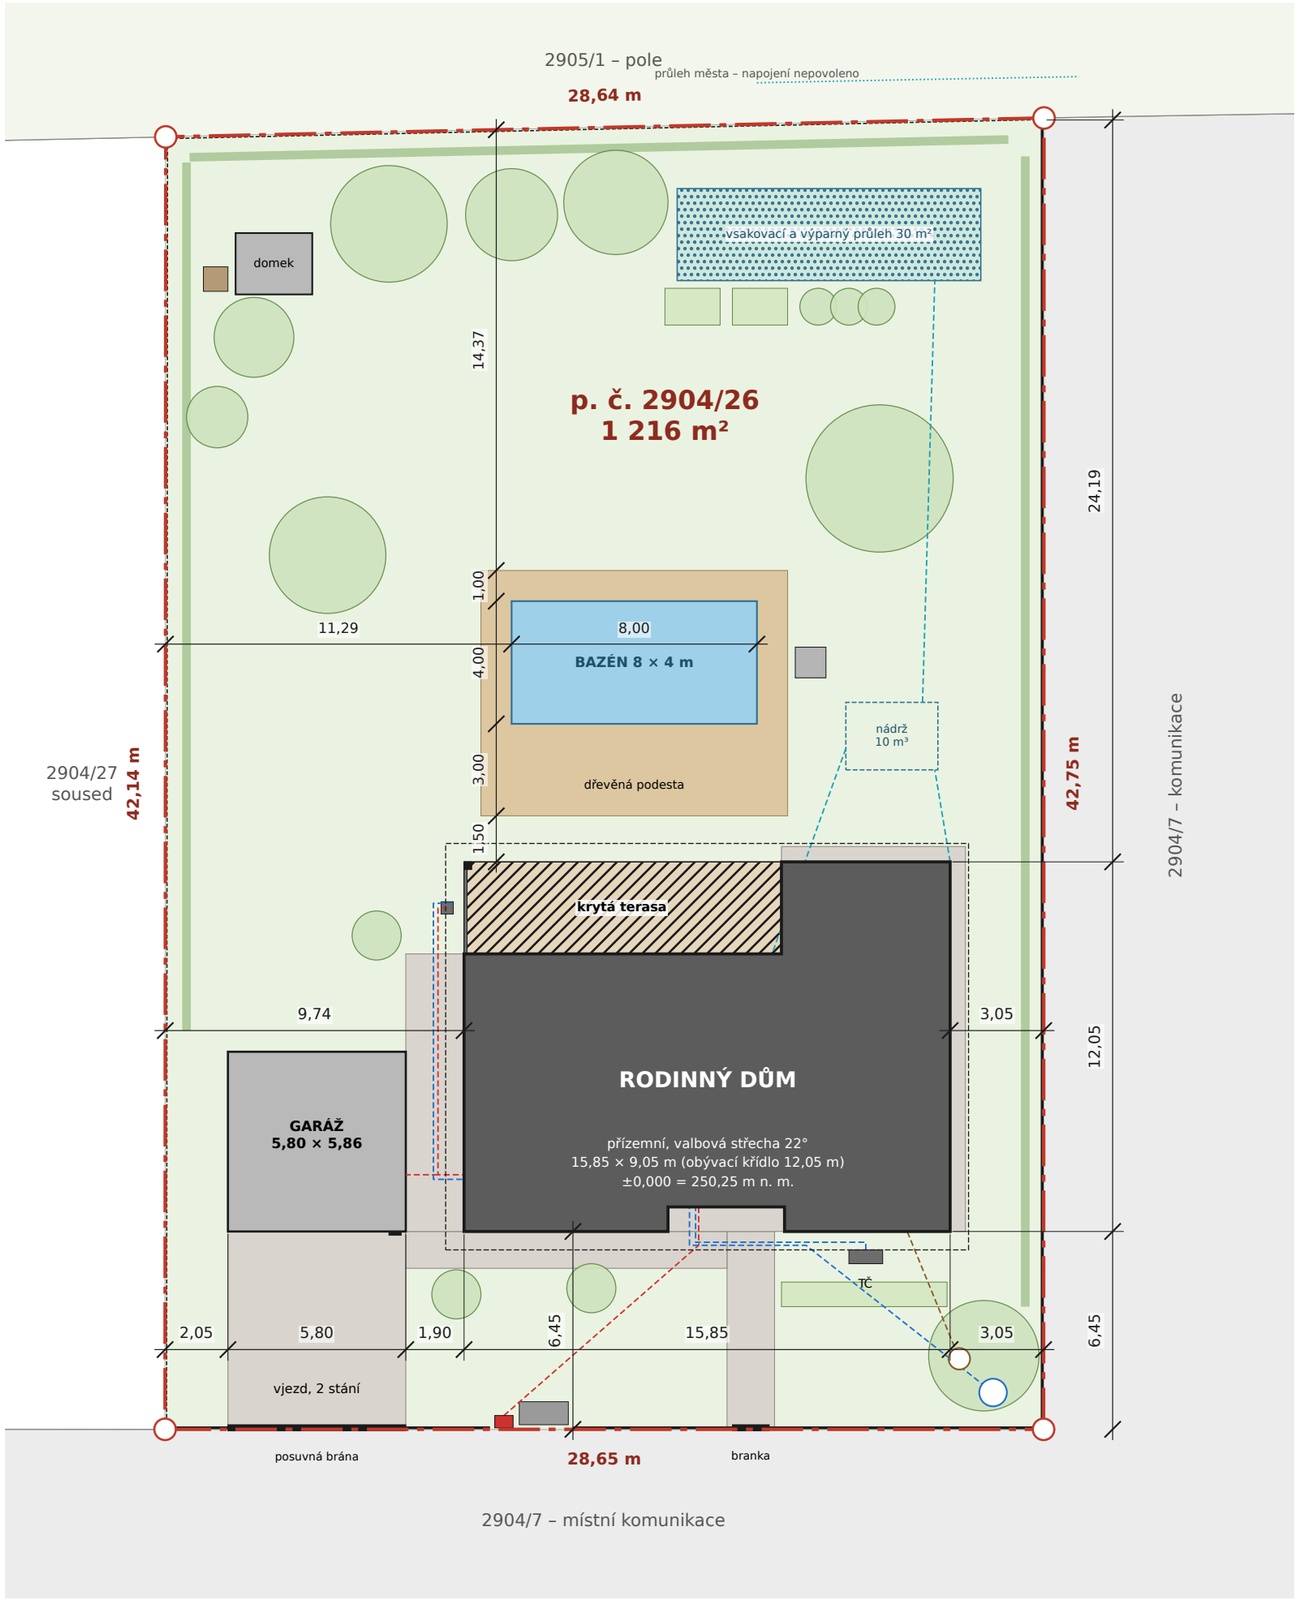


S

SITUACE

umístění domu na pozemku p. č. 2904/26

k. ú. Karviná-město · měřítko 1:200 (A3)

Plochy a odstupy

Pozemek p. č. 2904/26	**1 216 m²**
Dům (zastavěná plocha)	**156,90 m²**
Krytá terasa	**31,05 m²**
Garáž 5,80 × 5,86	**33,99 m²**
Zastavěnost dům + terasa + garáž	**221,9 m² = 18,3 % (max. 40 %)**
Index zastavění vč. zpevněných ploch	**398,6 m² = 32,8 % (max. 40 %)**
Zeleň	**817,0 m² = 67,2 % (min. 40 %)**
Bazén 8 × 4 m (drobná stavba)	**32,0 m²**
Odstup domu: jih (ulice)	**6,45 m**
Odstup domu: východ (komunikace)	**3,05 m**
Odstup domu: západ (soused)	**9,74 m, garáž 2,04 m**
Odstup domu: sever (pole)	**23,84 m**

Legenda

- hranice pozemku (katastrální mapa ČÚZK)
- rodinný dům
- garáž, zahradní domek
- krytá terasa
- zpevněné plochy (dlažba)
- bazén, kolem dřevěná podesta
- obrys střechy (přesah 0,60 m)
- plot do ulice: podezdívka + lamely 1,50 m
- plot k sousedům: pletivo 1,60 m
- živý plot
- elektro (pilíř na hranici)
- voda (vodoměrná šachta)
- kanalizace
- dešťová a užitková voda
- vsakovací a výparný průleh (zatravněný)

Rodinný dům Karviná – návrh v6 **1:200**

Situace – umístění stavby na pozemku

p. č. 2904/26, k. ú. Karviná-město · 25. 10. 2026

Kóty v metrech. Hranice podle katastrální mapy ČÚZK, nejde o geodetické zaměření.

Polohy přípojek a šachet jsou orientační. Orientační výkres, ne projektová dokumentace.